
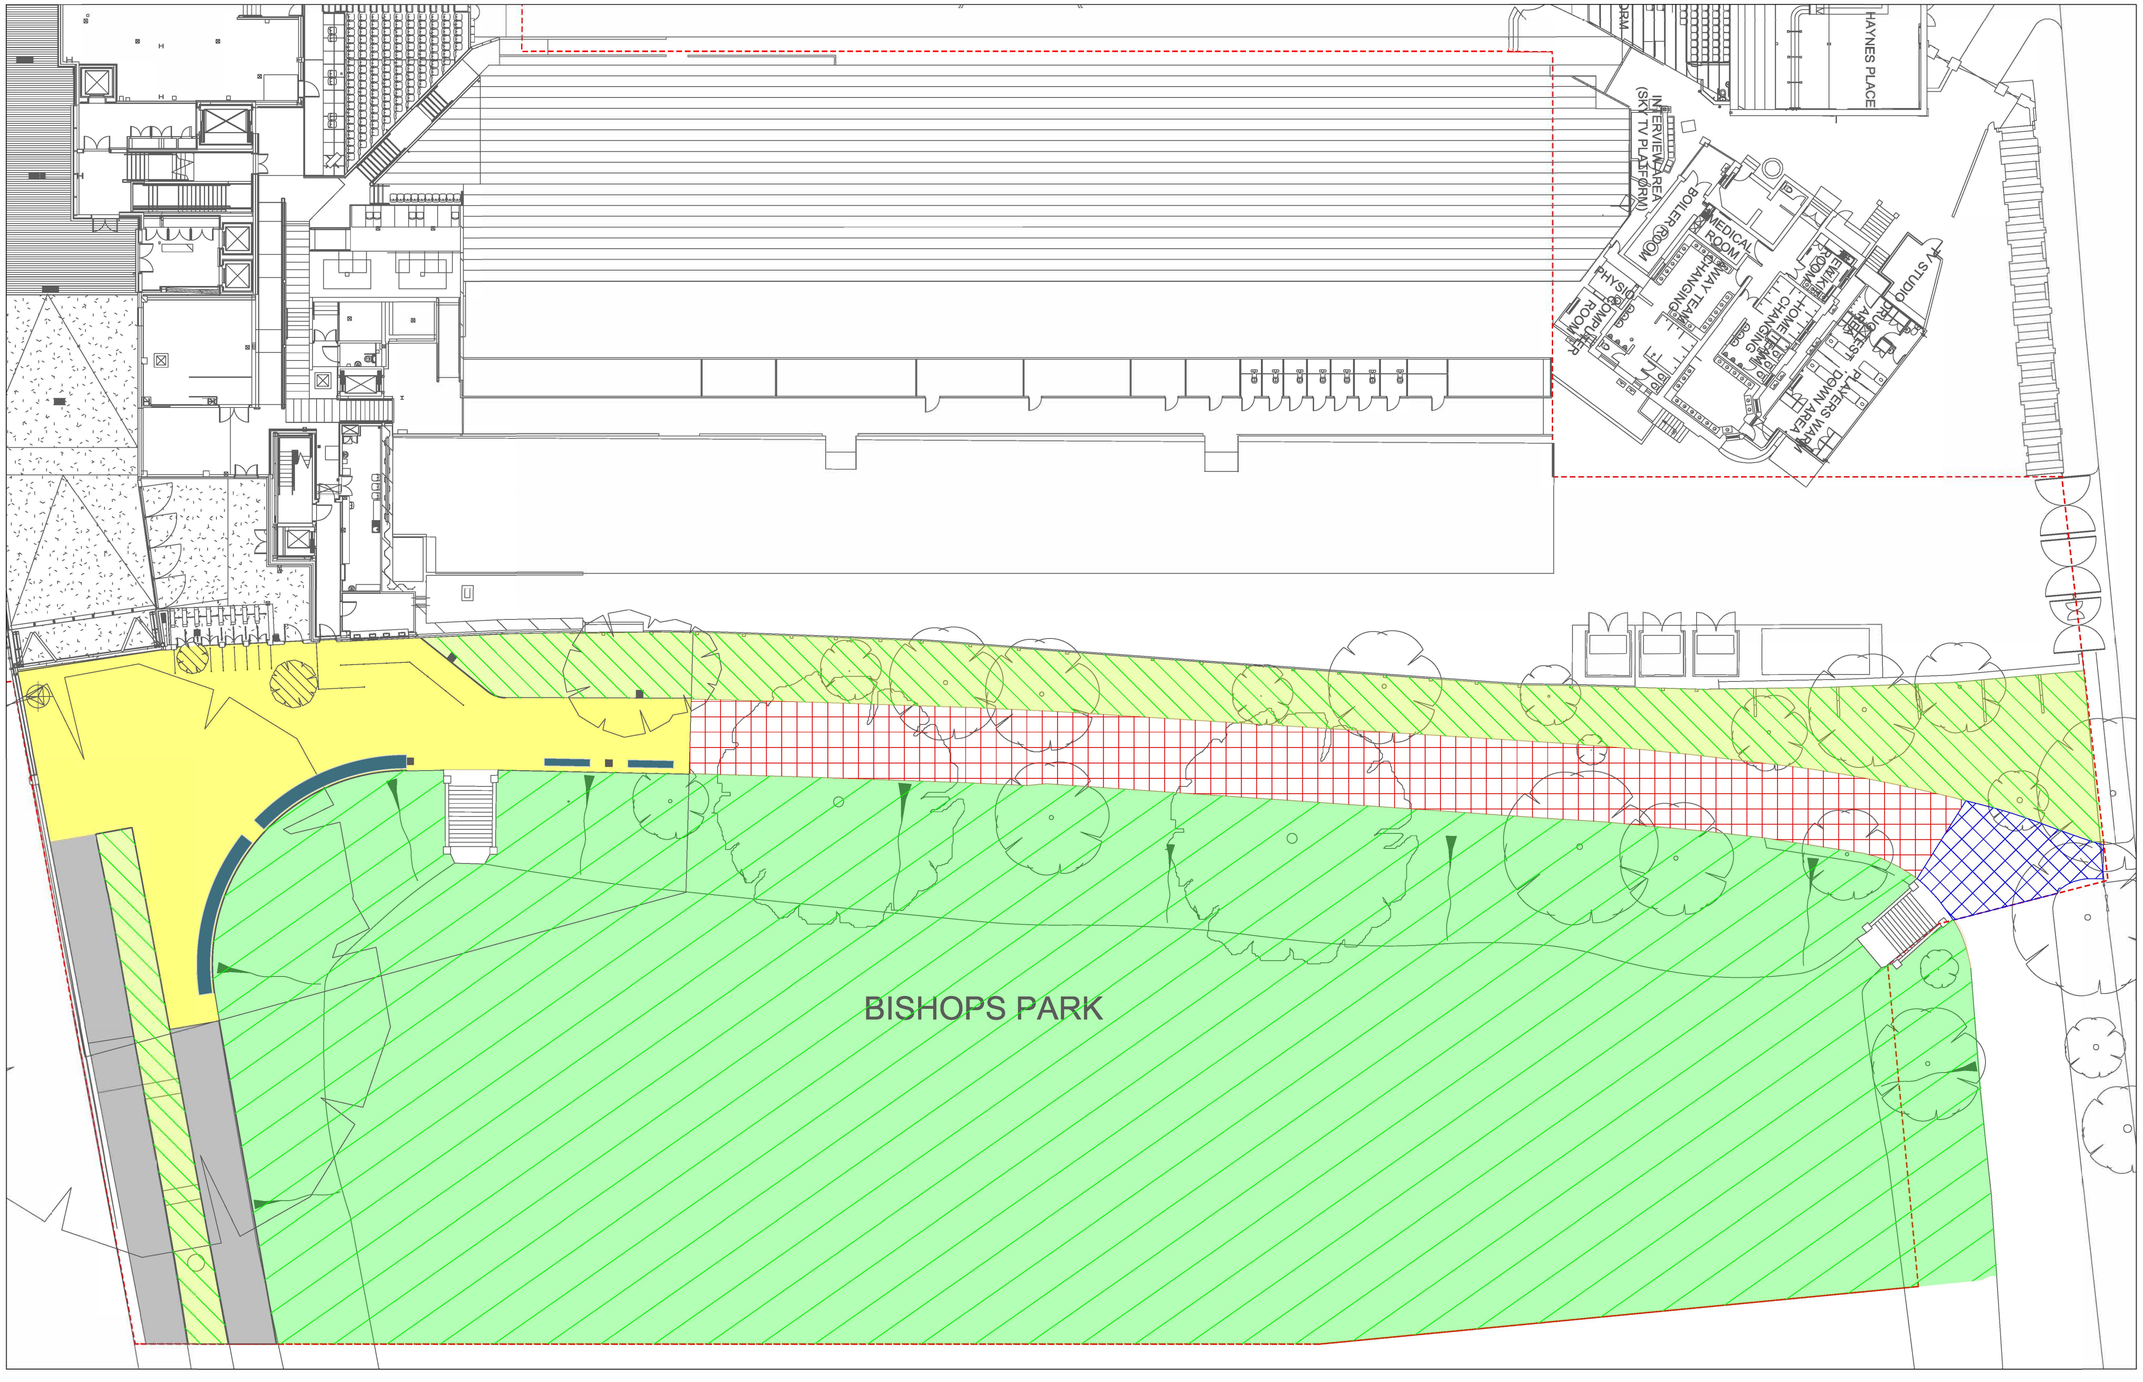


Do not scale from this drawing. All annotated dimensions must be checked on site prior to the commencement of any works and/ or the preparation of shop drawings. All sizes and positions of structural or services components are indicative only. Please refer to consultants' drawings and specifications for confirmation. This drawing should be read in conjunction with all relevant architect's drawings, specifications and other consultants' information.

© Copyright Stuart Forbes Associates Ltd, all rights reserved.

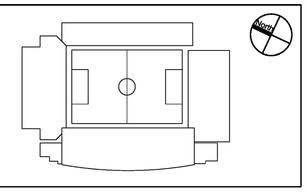

REV.	DATE	DESCRIPTION
13	28.06.2023	ISSUE FOR INFORMATION
14	11.09.2024	ISSUE FOR INFORMATION

LEGEND

- PLANNING APPLICATION BOUNDARY
- REPLACE 6MM ASPHALT WEARING COURSE
- REINSTATE ENTRANCE AREA WITH FOOTPATH CONSTRUCTION ASPHALT
- CEDEC GROUND COVERING TO MATCH EXISTING
- REINSTATE TARMAC SURFACE AS Per Specification
- FX-841 BENCHES
- EXISTING TREE TO BE REMOVED
- LAY NEW TURF/ RESEED EXISTING
- REINSTATE SOFT LANDSCAPING

Burlington Lodge Studios
Unit 2, Rigault Road
Fulham, London
SW6 4JJ
www.stuartforbes.com

Fulham Football Club Training Ground,
Motspur Park,
Surrey,
KT3 6PT

Project FULHAM PIER RIVERSIDE STAND

Drawing Name **Bishop's Park Reinstatement Plan Drawing**

Job No. 2004 **Scale** 1:200@A1 **Date** JUN 2023

Drawing No. FFC-SFA-XX-00-DR-W-016 **Rev.** 14